
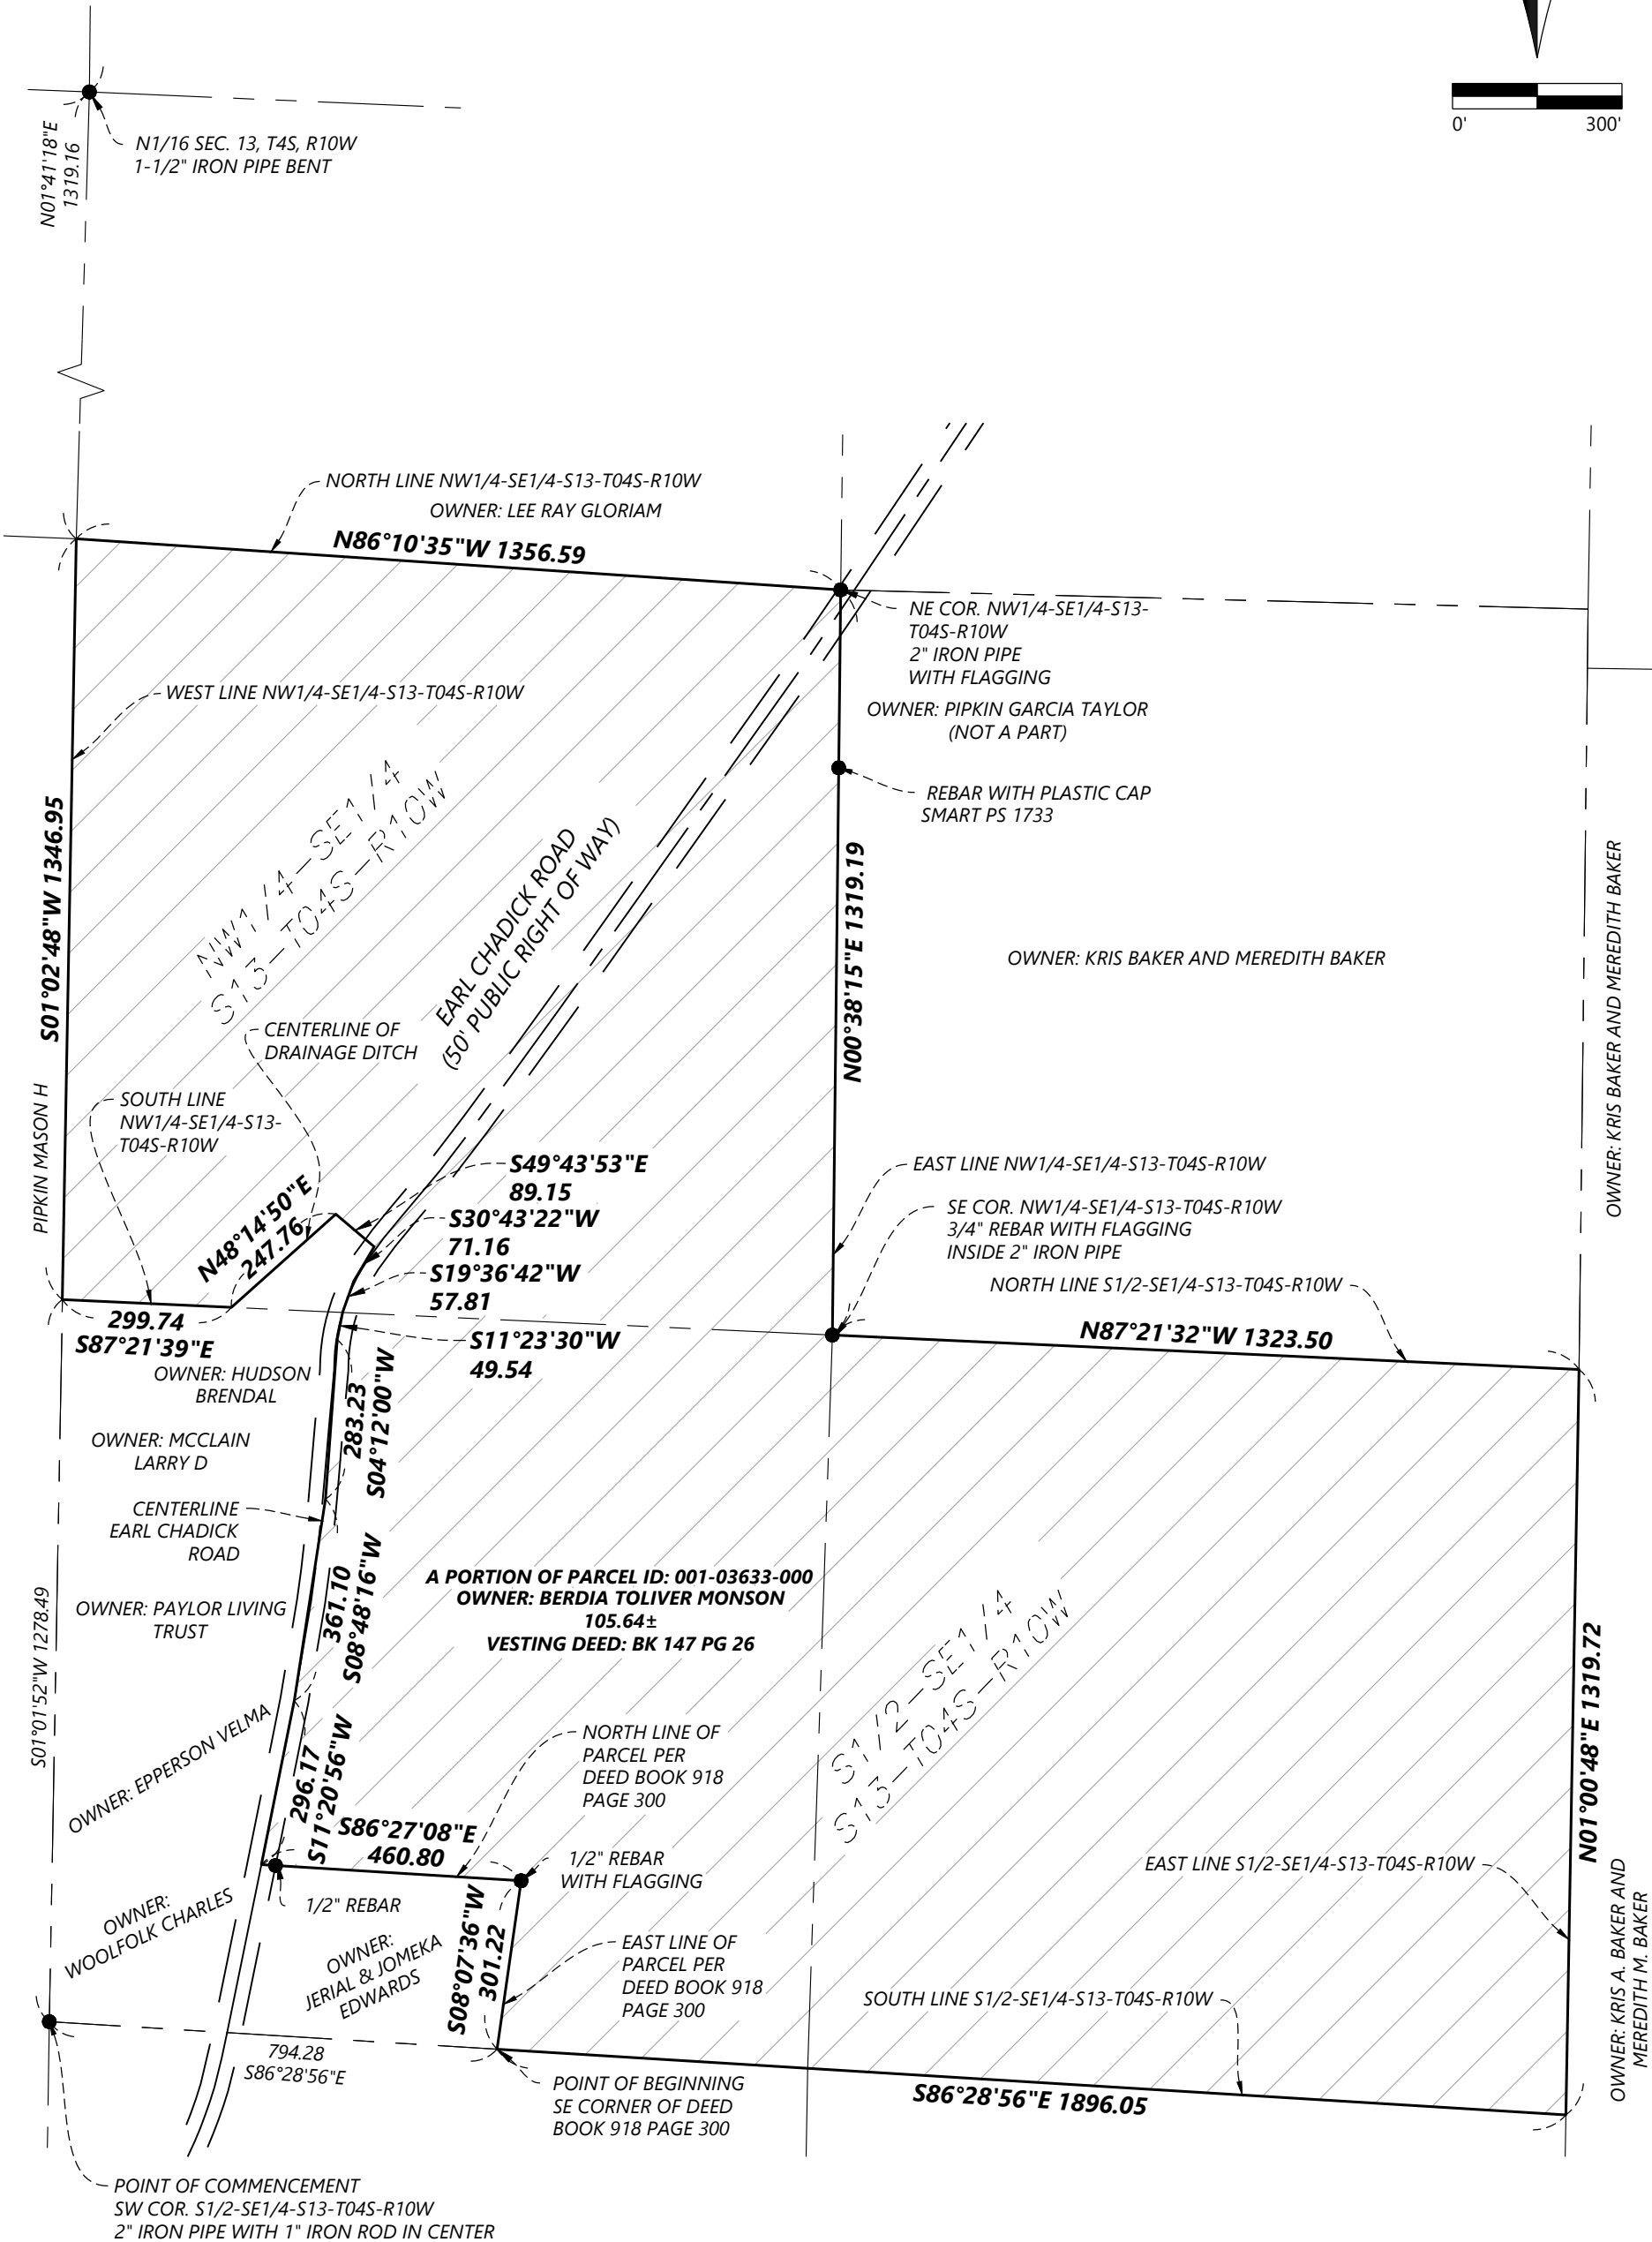


Legend

- FOUND MONUMENT
- SECTION LINE
- RIGHT OF WAY LINE
- PARCEL LINE
- DESCRIBED AREA

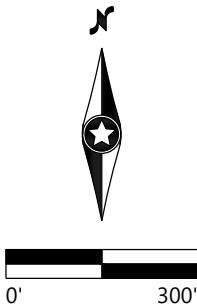

Phone (952) 937-5150 12701 Whitewater Drive, Suite #300
Toll Free (888) 937-5150 Minnetonka MN, 55343
westwoodps.com

Westwood Professional Services, Inc.

Plum Bayou Solar

Jefferson County, Arkansas

Area Description
Exhibit

DATE: 03/05/2026

SHEET: 01 of 02

PARENT TRACT DESCRIPTION (PID: 001-03633-000)

The Northwest Quarter (NW ¼) of the Southeast Quarter (SE ¼); and the South Half (S ½)of the Southeast Quarter (SE ¼) all in Section 13, Township 4 South, Range 10 West of the 5th P.M.;

LESS AND EXCEPT, A parcel of land located in the Southwest Quarter(SW¼)of the Southeast Quarter (SE¼) of Section 13, Township 4 South, Range 10 West of the 5th P. M., within the following boundaries, to-wit: Begin at a point 50 feet North and 302 feet East of the Southwest corner of the Southwest Quarter (SW ¼) of the Southeast Quarter (SE ¼) of said Section 13 run thence North 63 degrees 30 minutes West, a distance of 115.3 feet; thence North 44 degrees 15 minutes West, a distance of 102 feet, thence North 5 degrees West, a distance of 168 feet, thence South 78 degrees 45 minutes East, a distance of 239 feet, thence South 10 degrees 45 minutes West, a distance of 249 feet to the point of beginning;

AND ALSO, LESS AND EXCEPT, A part of the Southwest Quarter (SW ¼) of the Southeast Quarter (SE ¼) of Section 13, Township 4 South, Range 10 West of the 5th P.M., more particularly described as follows: Commencing at the Southwest corner thereof; thence running East 302 feet; thence North 50 feet; thence North 10 degrees 45 minutes East 299 feet to the point of beginning; thence running North 78 degrees 45 minutes West 239 feet; thence running North 5 degrees West 145 feet; thence running South 78 degrees 45 minutes East 284 feet; thence running South 10 degrees 45 minutes West 200 feet to the point of beginning;

AND ALSO, LESS AND EXCEPT, A part of the Southwest Quarter (SW¼) of the Southeast Quarter (SE ¼) of Section 13, Township 4 South, Range 10 West of the 5thP. M., thence beginning at the Southwest corner of the Southwest Quarter (SW ¼) of the Southeast Quarter (SE ¼); thence East 302 feet to the center of county road, thence in a Northeasterly direction 600 feet for a point of beginning, thence West 312 feet; thence North 280 feet; thence East 361 feet to the center of County road; thence South westerly along county road a distance of 280 feet to the point of beginning;

AND ALSO, LESS AND EXCEPT, Commencing at the Southwest corner of the Southeast (SE ¼) of Section 13, Township 4 South, Range 10 West of the 5th P. M., said point being an iron pin set by J. H. Gould; thence running in an Easterly direction, 302 feet, plus or minus, to the centerline of a bridge over the “Main Canal”, said point being in the centerline of Pastoria-Wright Road (also known as Jefferson County Road No. 73-NKA Earl Chadick Road); thence North 10 degrees 30 minutes East along and with said center line 960 feet to the point of beginning, said point being a railroad spike in the centerline of said road; thence North 86 degrees 30 minutes West 450 feet to a point; said point being in the centerline of “Main Canal”; thence North 1 degree East along and with the centerline of said canal 200 feet, to a point, said point being the intersection of a drainage ditch with the “Main Canal”; thence Northeasterly, along and with the center line of the drainage ditch 530 feet, plus or minus, to a point; thence South 56 degrees East 92 feet to a point in the centerline of said County Road; thence Southwesterly along and with the centerline of said County Road 160 feet to a point; thence South 5 degrees 30 minutes West, along and with the centerline of said County Road, 290 feet to the point of beginning;

AND ALSO, LESS AND EXCEPT, Part of the Southwest Quarter (SW ¼) of the Southeast Quarter (SE ¼) of Section 13, Township 4 South, Range 10 West of the 5th P. M., Jefferson County, Arkansas, described as follows: Commence at the Southwest corner of the Southeast Quarter (SE ¼) of said Section 13,thence East for a distance of 315.20 feet to the intersection of the center of a county road and the drainage canal for the point of beginning; thence North 08 degrees 07 minutes 36 seconds East for a distance of 300 feet along the center of Earl Chadick Road; thence East a distance of 460.43 feet; thence South 08 degrees 07 minutes 36 seconds West for a distance of 300 feet to the center of the canal; thence North 90 degrees 00 minutes 00 seconds West for a distance of 460.43 feet to the point of beginning.

AREA DESCRIPTION

A portion of the Northwest Quarter (NW ¼) of the Southeast Quarter (SE ¼); and the South Half (S ½) of the Southeast Quarter (SE ¼) all in Section 13, Township 04 South, Range 10 West of the 5th P.M., County of Jefferson, State of Arkansas, more particularly described as follows:

Commencing at the southwest corner of said South Half of the Southeast Quarter; thence South 86 degrees 28 minutes 56 seconds East along the south line of said South Half of the Southeast Quarter, a distance of 794.28 feet to the southeast corner of a parcel as recorded in Deed Book 918, Page 300 also being the Point of Beginning; thence continue South 86 degrees 28 minutes 56 seconds East along said south line, a distance of 1,896.05 feet to the east line of said South Half of the Southeast Quarter; thence North 01 degree 00 minutes 48 seconds East along said east line, a distance of 1,319.72 feet to the north line of said South Half of the Southeast Quarter; thence North 87 degrees 21 minutes 32 seconds West, a distance of 1,323.50 feet to the southeast corner of said Northwest Quarter of the Southeast Quarter; thence North 00 degrees 38 minutes 15 seconds East along the east line of said Northwest Quarter of the Southeast Quarter, a distance of 1,319.19 feet to the northeast corner of the said Northwest Quarter of the Southeast Quarter; thence North 86 degrees 10 minutes 35 seconds West along the north line of said Northwest Quarter of the Southeast Quarter, a distance of 1,356.59 feet to the west line of said Northwest Quarter of the Southeast Quarter; thence South 01 degree 02 minutes 48 seconds West along said west line, a distance of 1,346.95 feet to the south line of said Northwest Quarter of the Southeast Quarter; thence South 87 degrees 21 minutes 39 seconds East along said south line, a distance of 299.74 feet; thence North 48 degrees 14 minutes 50 seconds East, along the centerline of a drainage ditch, a distance of 247.76 feet; thence South 49 degrees 43 minutes 53 seconds East, a distance of 89.15 feet to the centerline of Earl Chadick Road; thence following the centerline for the following six courses:

thence South 30 degrees 43 minutes 22 seconds West, a distance of 71.16 feet;
thence South 19 degrees 36 minutes 42 seconds West, a distance of 57.81 feet;
thence South 11 degrees 23 minutes 30 seconds West, a distance of 49.54 feet;
thence South 04 degrees 12 minutes 00 seconds West, a distance of 283.23 feet;
thence South 08 degrees 48 minutes 16 seconds West, a distance of 361.10 feet;
thence South 11 degrees 20 minutes 56 seconds West, a distance of 296.17 feet, to the north line of said parcel recorded in Deed Book 918, Page 300;

thence leaving said centerline South 86 degrees 27 minutes 08 seconds East along said north line, a distance of 460.80 feet to the east line of said parcel; thence South 08 degrees 07 minutes 36 seconds West, along said east line, a distance of 301.22 feet to the Point of Beginning.

Containing 4,601,617 square feet or 105.64 acres, more or less.

All bearings, distances, and areas shown hereon are grid and based on the NAD83(2011) Arkansas State Coordinate System, South Zone, US Survey Foot.

N:\036023.00_CAD_Survey\EXHIBITS\Area Exhibits\046023V-LS-03 AR-WBT-1-120.dwg